



L'ARCHITECTURE AU SERVICE DE L'AMBITION

UN ENSEMBLE UNIVERSITAIRE CLASSÉ AU PATRIMOINE DU XXÈME SIÈCLE

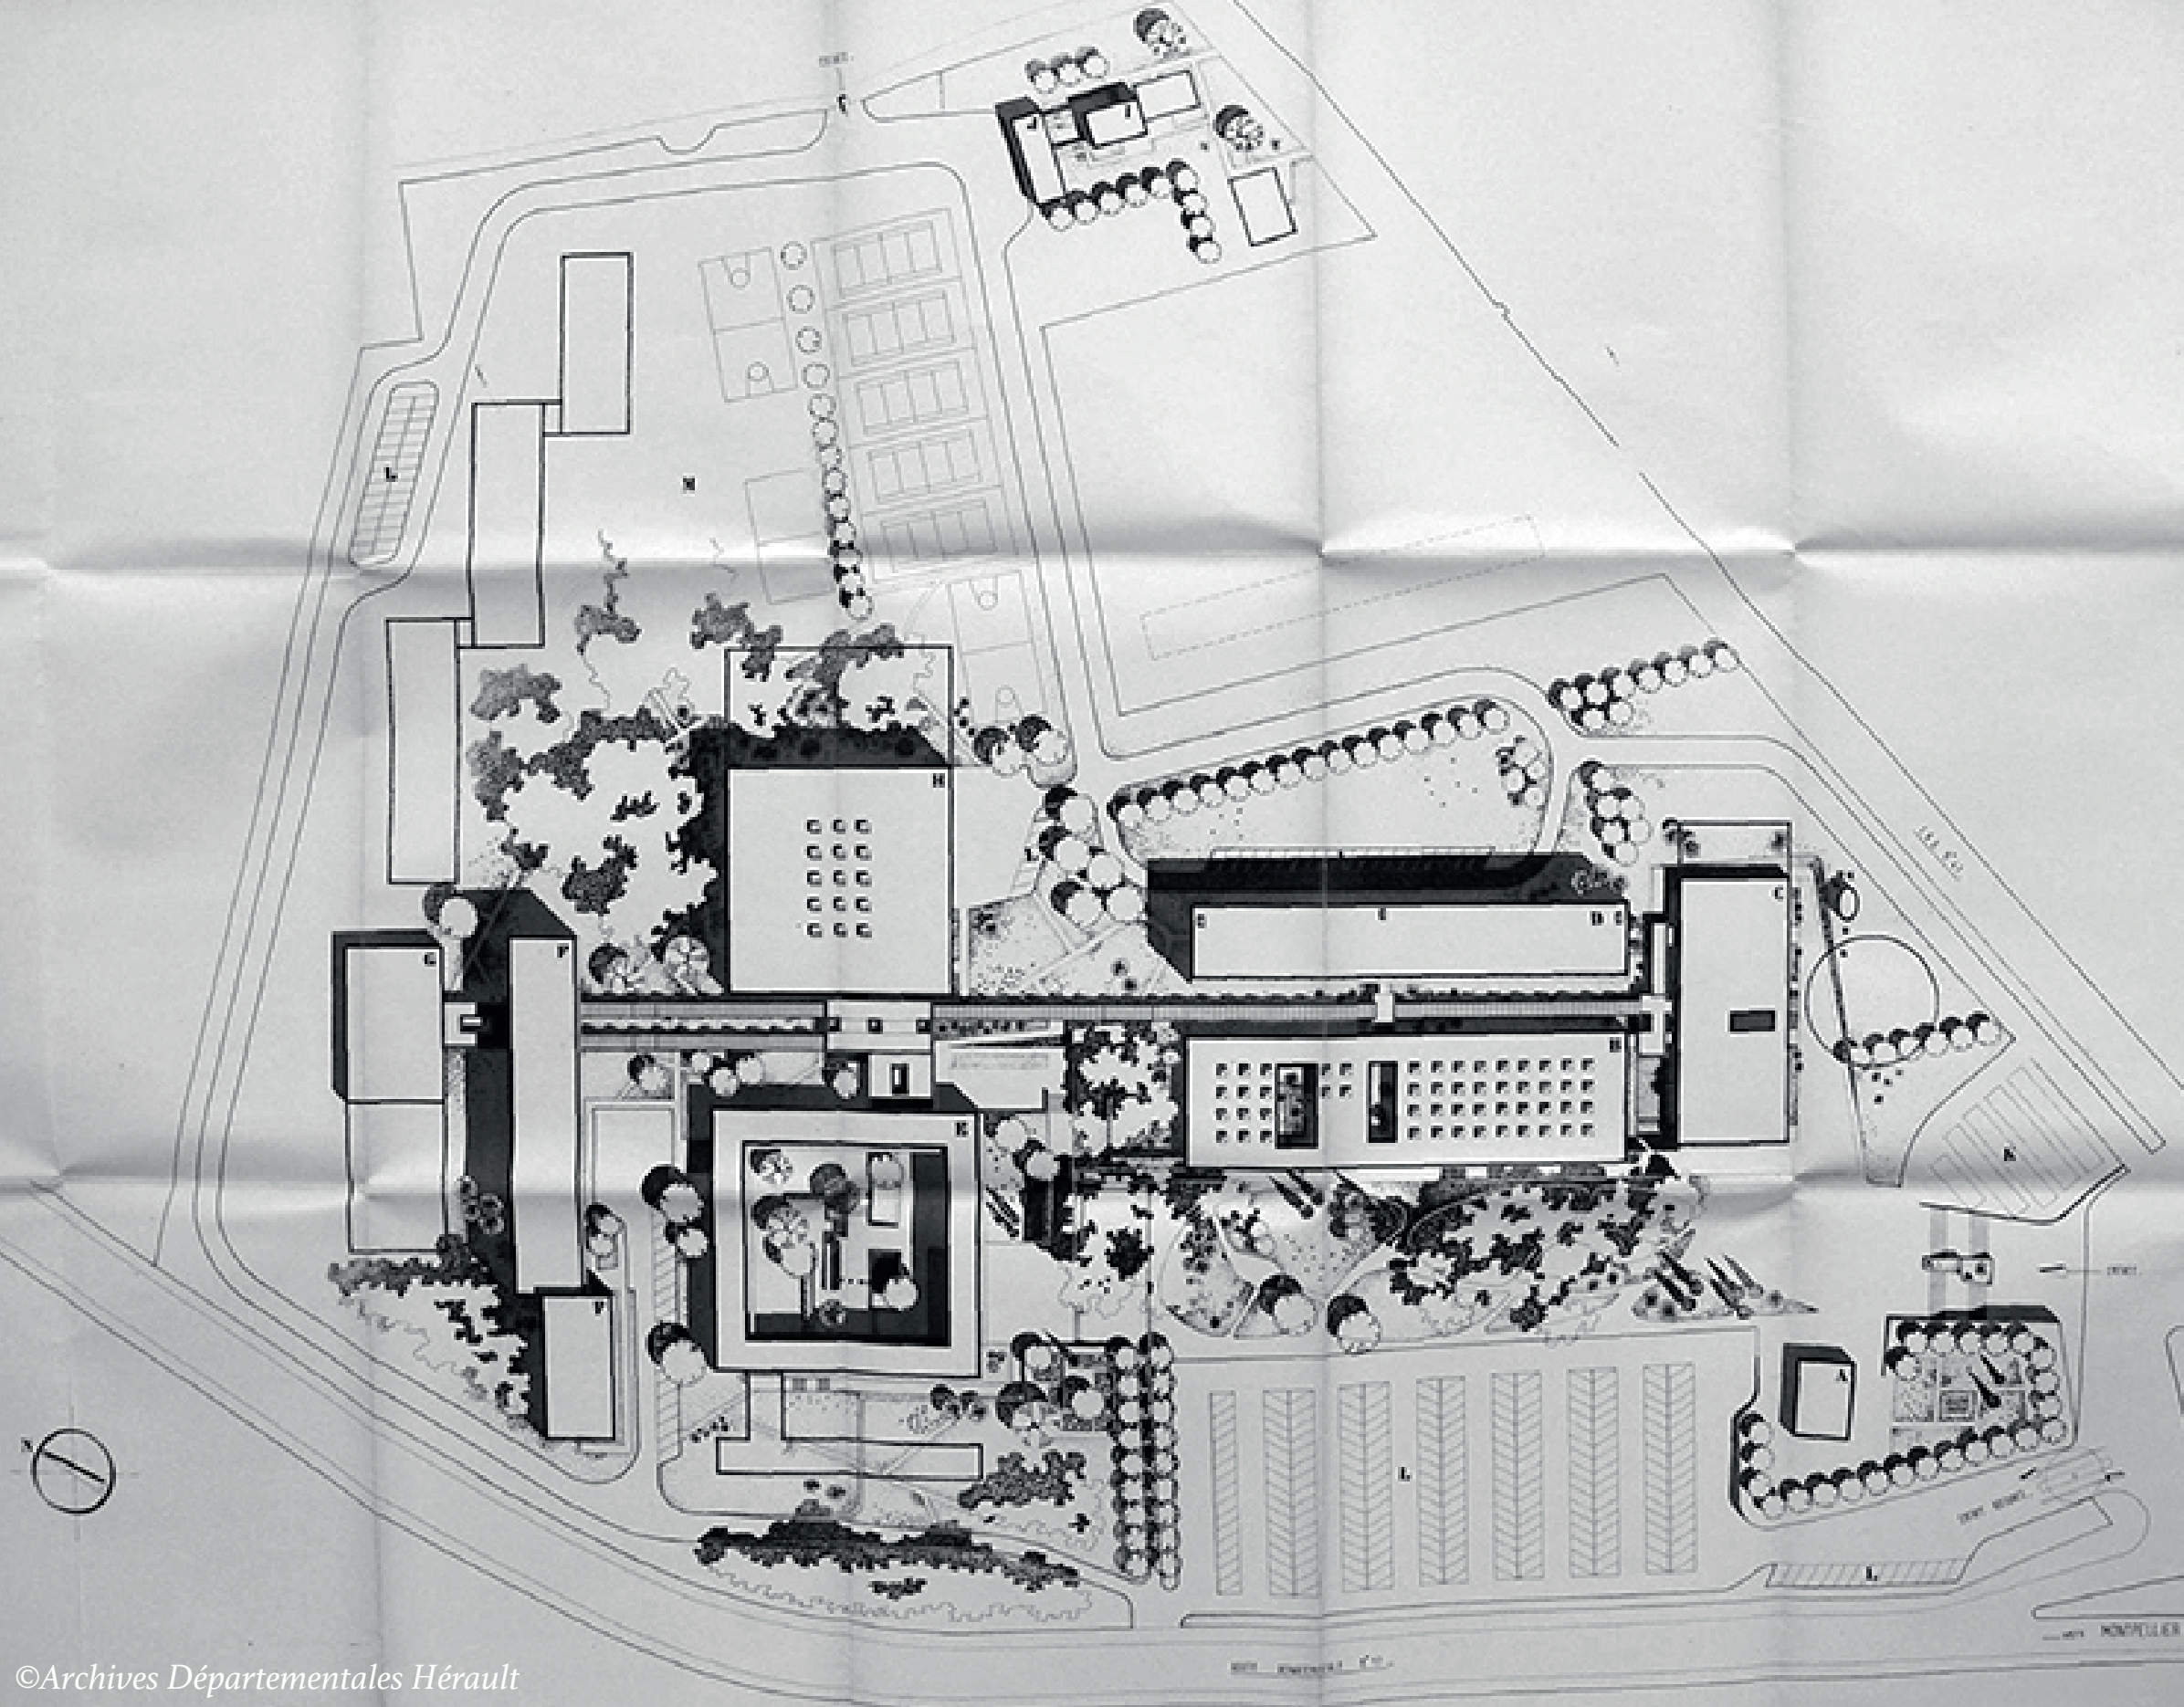

©Archives Départementales Hérault
Plan de masse de la faculté des Lettres, 1963.

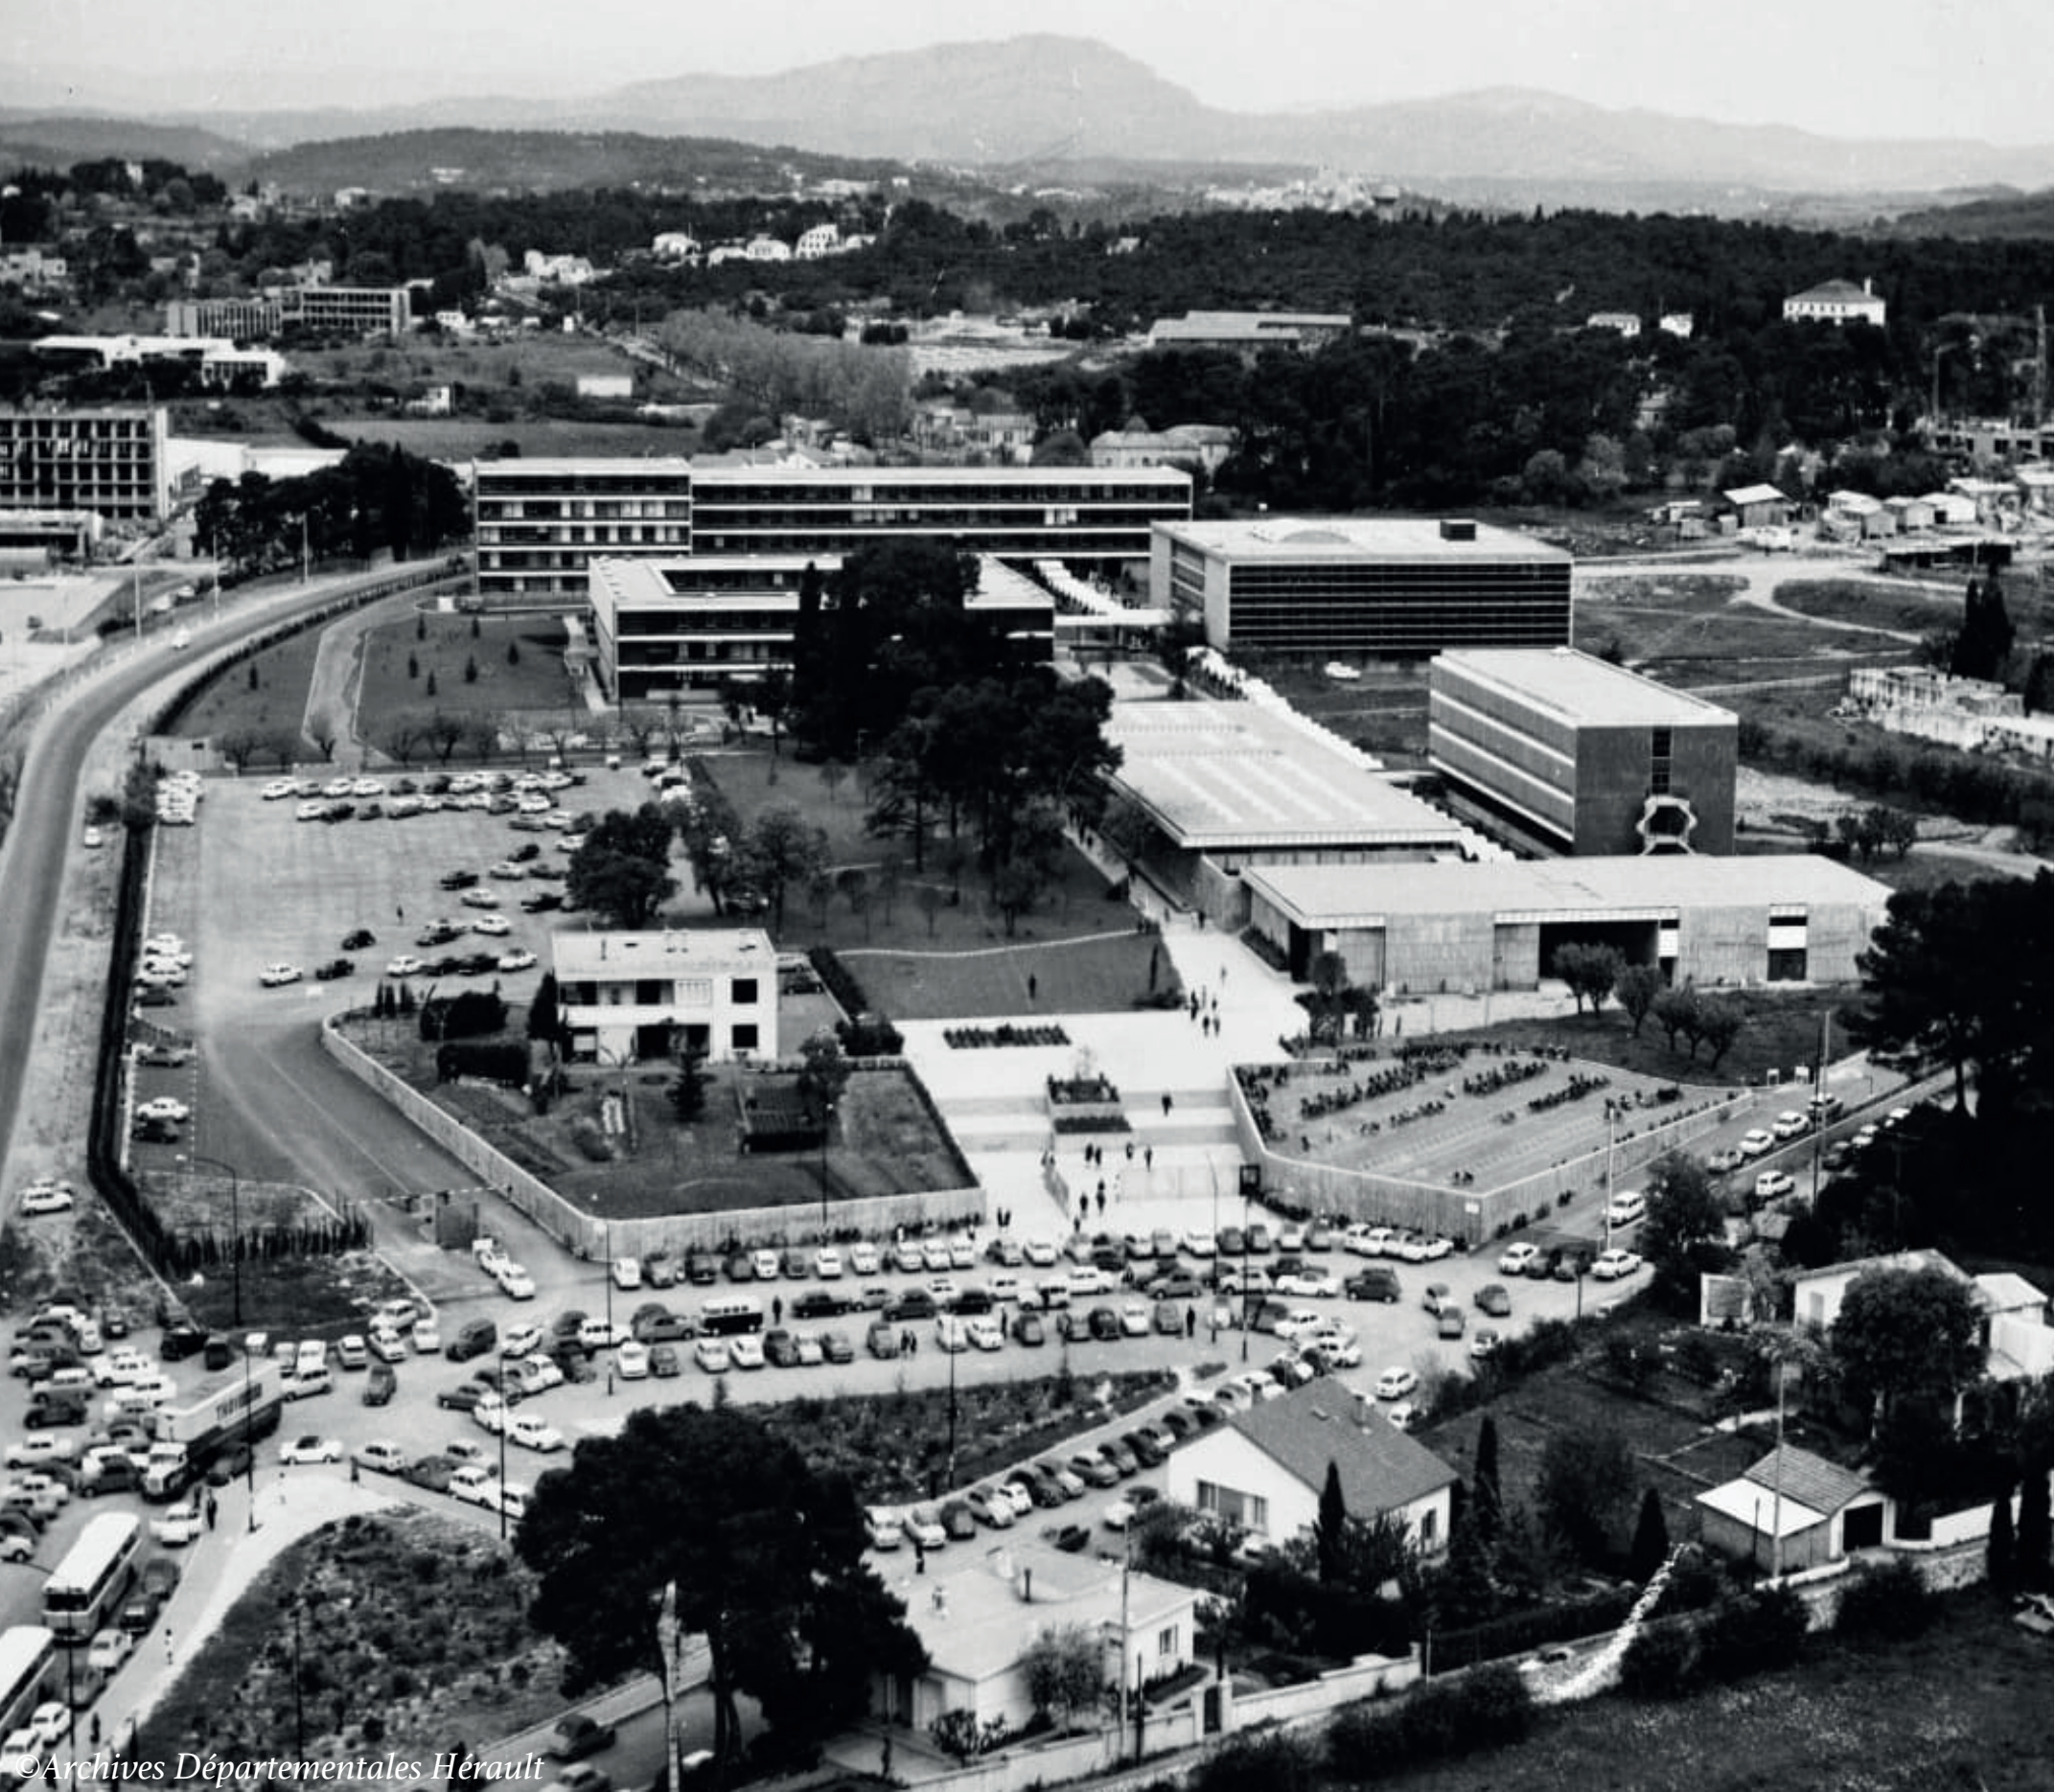

©Archives Départementales Hérault
Le site universitaire de Paul-Valéry en 1966.

RÉPONDRE À UN BESOIN

Avant 1963, le nouveau « campus de Montpellier » est construit sans plan global, au rythme des besoins. René Egger répond à une urgence par une architecture fonctionnelle et normalisée. Malgré la qualité des bâtiments, le manque d'unité, la coupure du site et l'éloignement des logements empêchent la création d'un campus cohérent.

10 ANS DE CONSTRUCTION POUR 8 600 ÉTUDIANTS

1956 FACULTÉ EN CENTRE-VILLE

La faculté des Lettres et Sciences humaines de Montpellier, située rue du Cardinal de Cabrières, accueille 1 500 étudiants, alors que le bâtiment inauguré en 1939 avait été conçu pour en recevoir seulement 600.

1958 DÉPLACEMENT VERS LE NORD

La décision est prise de construire un nouveau complexe universitaire au nord de Montpellier, après l'acquisition de terrains appartenant à 36 propriétaires différents.

1961 1^{ER} PLAN DE L'UNIVERSITÉ


En janvier, le programme pédagogique de la Faculté des Lettres et Sciences humaines est défini pour accueillir 8 600 étudiants en 1965-1966. Le plan masse est validé. En 1961, la conception est confiée à René Egger, assisté par l'agence Jaulmes et Deshons.

1966 LIVRAISON

Le 15 octobre, les nouveaux bâtiments accueillent leur première rentrée universitaire. D'autres bâtiments sortent de terre par la suite.



©Archives Départementales Hérault
Ancien portique entre la bibliothèque et les salles de travail (aujourd'hui bâtiment de l'administration).

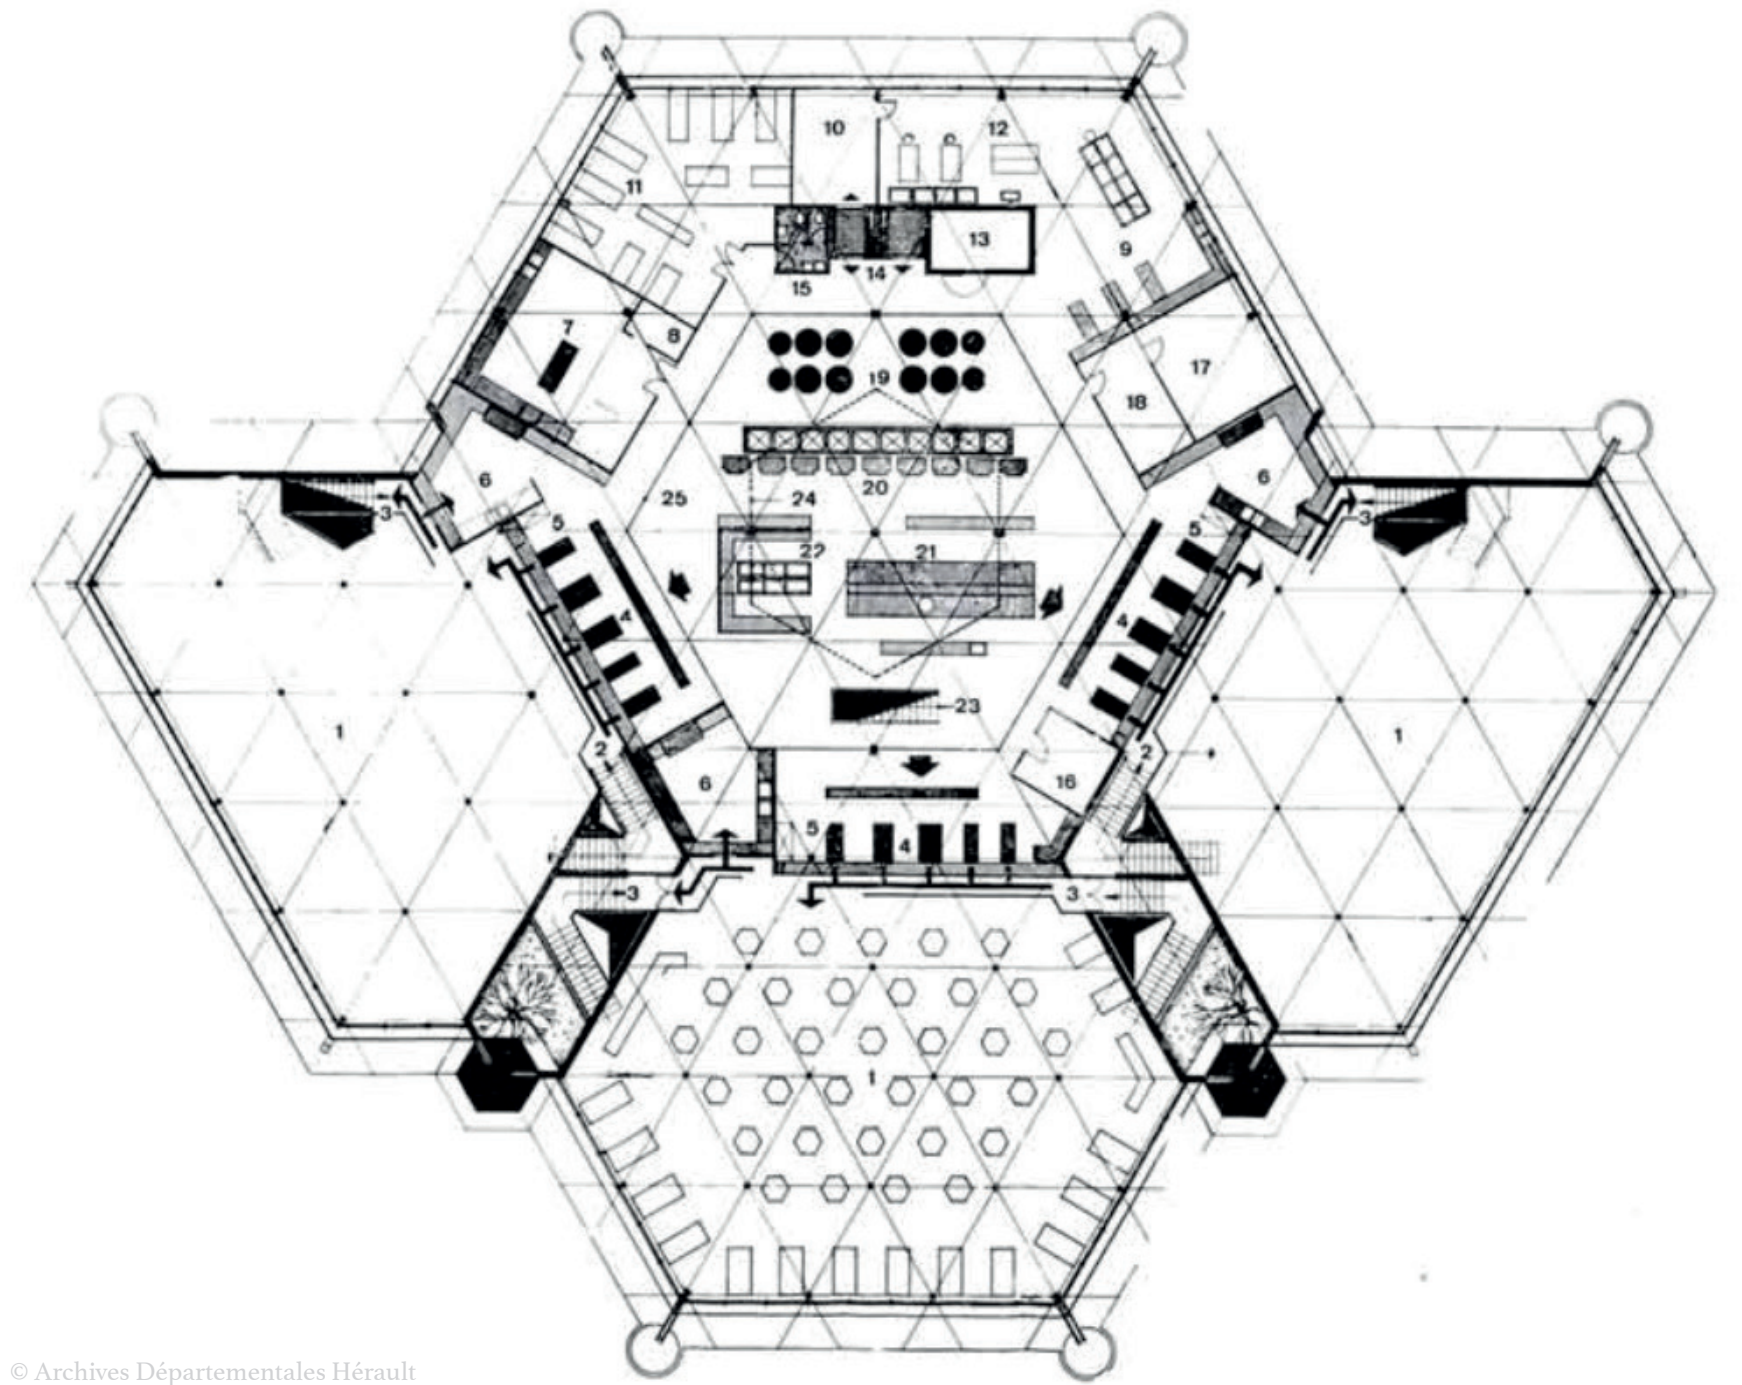

©Archives Départementales Hérault
Plan de l'étage du restaurant universitaire Vert Bois en 1967 réalisé par Philippe Jaulmes et Jean-Claude Deshons.



©Archives Départementales Hérault
Allée centrale, axe Nord-Sud, articulant le site universitaire, réalisé par Philippe Jaulmes en 1966.



©Archives Départementales Hérault
Le bâtiment de l'administration et des salles de travail avec le jardin du labyrinthe au premier plan.

CARACTÉRISTIQUES ARCHITECTURALES

ARCHITECTURE MODERNE

L'architecture moderne se fonde sur le fonctionnalisme, l'innovation constructive et la rationalisation de l'espace. Elle privilégie structure lisible, plan libre et lumière naturelle, en réponse aux transformations sociales, industrielles et technologiques du XX^e siècle. (Frampton, 1980 ; Curtis, 1996)

LECTURE DU SITE UNIVERSITAIRE PAUL-VALÉRY

Le site adopte d'abord un style néoclassique, puis évolue vers une architecture plus moderne et fonctionnelle. Les bâtiments sont conçus en lien avec le site, en respectant le relief, la végétation et les contraintes de la ville. Leur hauteur est volontairement limitée. L'ensemble est pensé comme un campus fermé sur lui-même, organisé autour d'une allée piétonne centrale. Les déplacements internes et les espaces calmes sont privilégiés, tandis que la voiture - au début du moins - est tenue à distance. L'architecture est guidée avant tout par les besoins pédagogiques. L'entrée monumentale et la présence de l'art contemporain expriment une volonté symbolique et culturelle.

REVALORISATION ARCHITECTURALE ET PATRIMONIALE

2008 OPÉRATION CAMPUS


Lancée par l'État, il vise à moderniser les infrastructures universitaires pour créer des campus attractifs et visibles à l'international. Doté de financements importants, il privilégie la réhabilitation des campus existants, surtout ceux des années 1960-1970, en respectant leur valeur architecturale et en soutenant l'autonomie des universités.

2011 ARCHITECTURE CONTEMPORAINE REMARQUABLE

Le ministère de la Culture a mis en place un label pour reconnaître et faire connaître le patrimoine du XX^e siècle. L'université Paul-Valéry a obtenu cette labellisation qui valorise ses qualités architecturales et paysagères. Ce label, sans valeur juridique, sert à sensibiliser le public, favoriser la transmission de cet héritage, soutenir la gestion du campus et renforcer son image culturelle.



©Archives Départementales Hérault
Long mur cyclopéen du musée des moulages réalisé par le plasticien Albert Dupin à base de pierres volcaniques de la région de Clermont-l'Hérault.

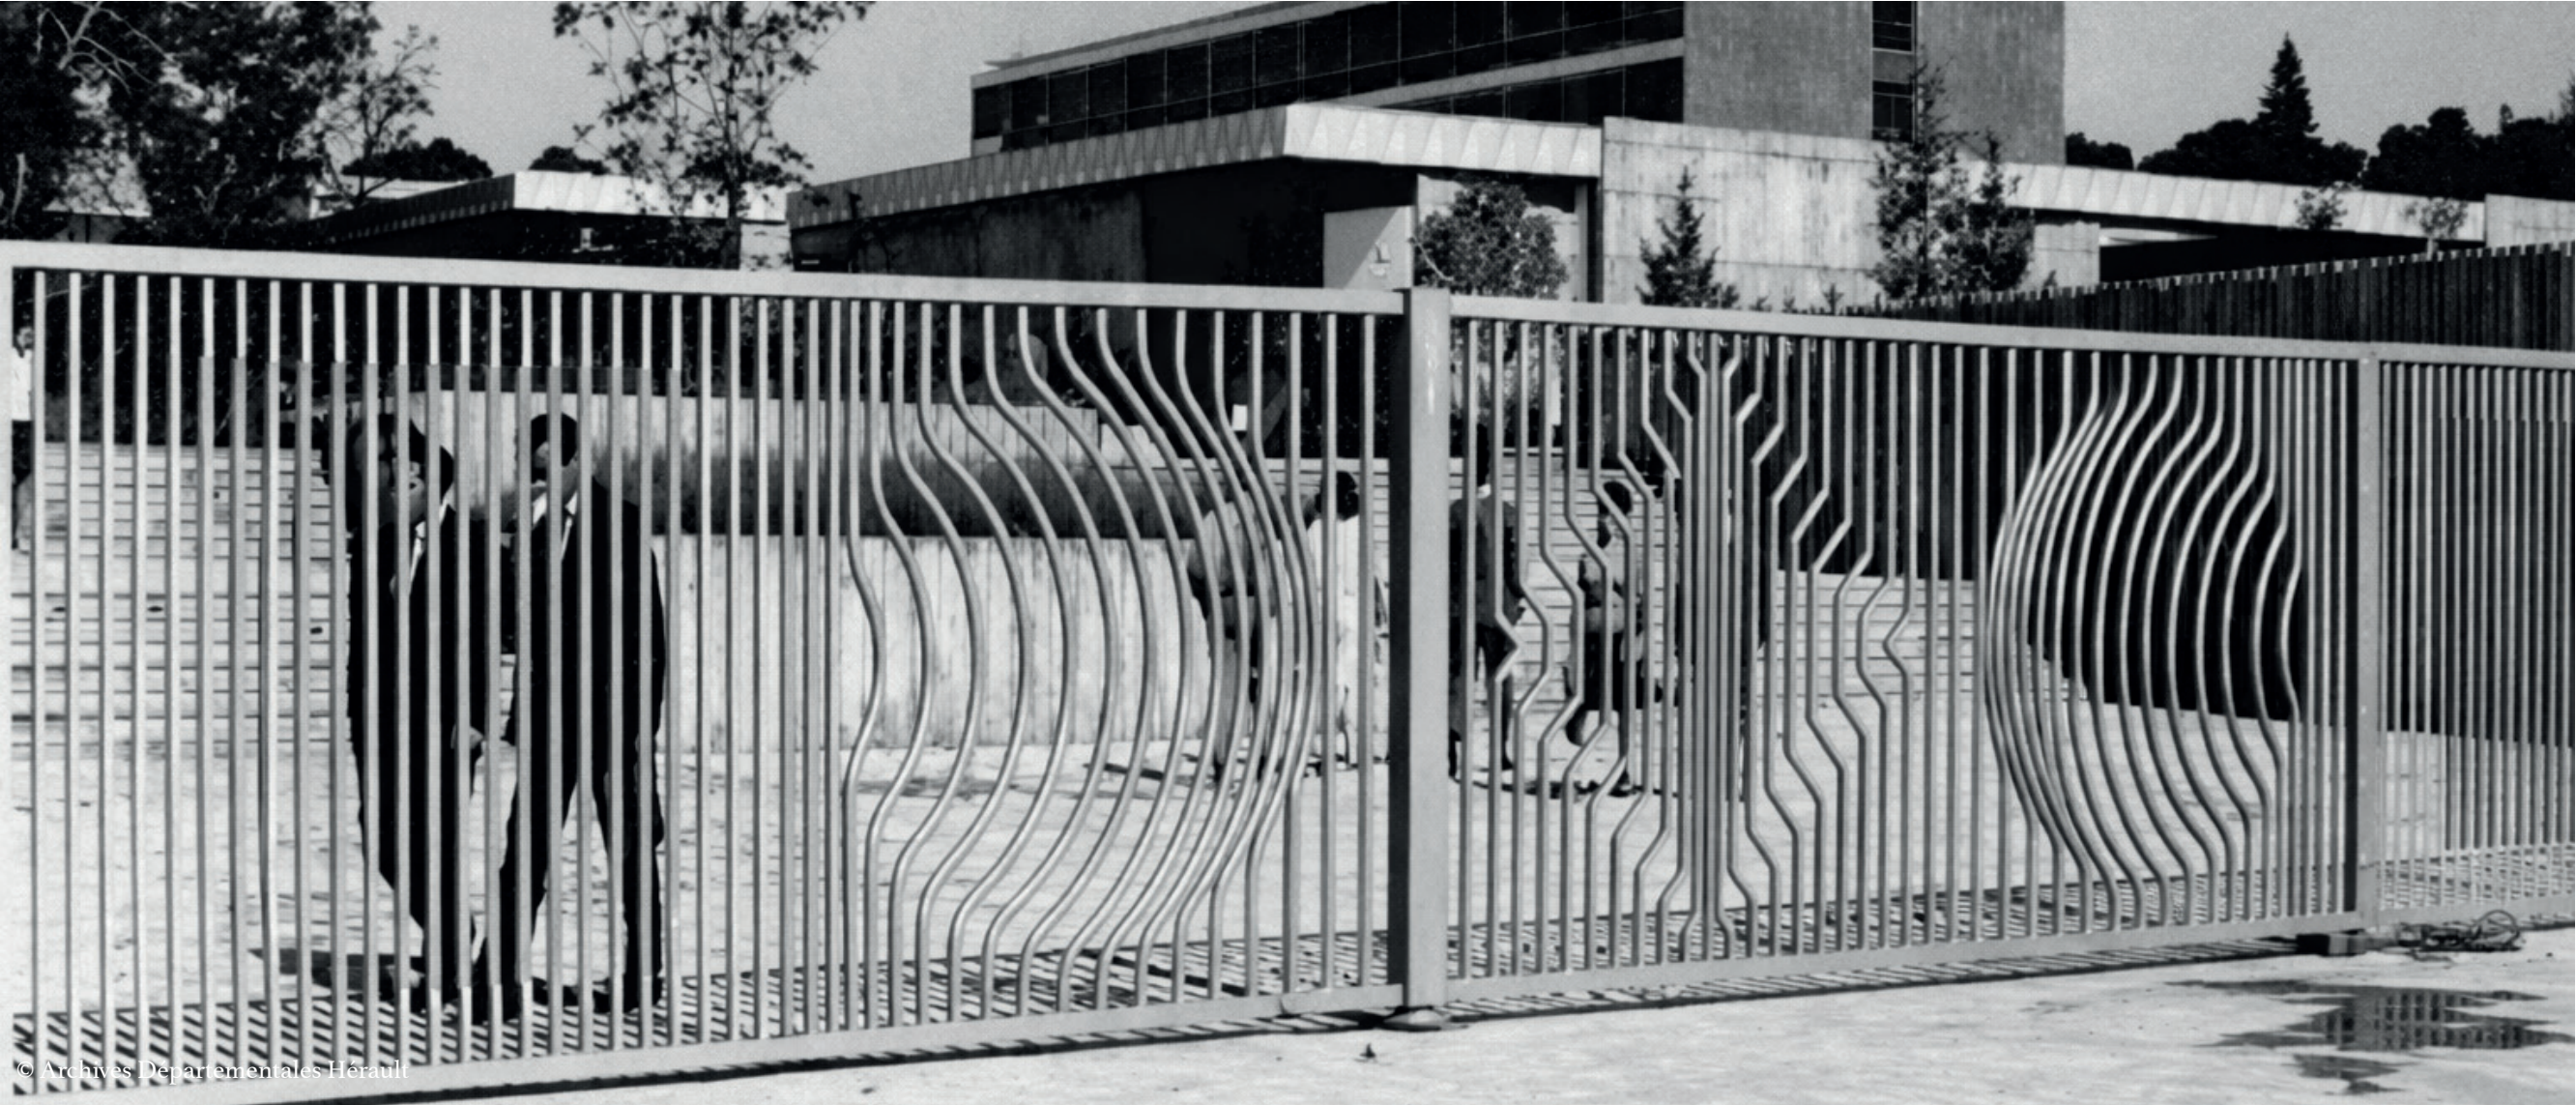

Le portail monumental en métal, réalisé par Victor Vasarely en 1966.



©Archives Départementales Hérault
Spirale du grand escalier en tubulures métalliques par Philippe Jaulmes de l'ancienne bibliothèque universitaire.

EN SAVOIR +

« Un équipement public, il n'est pas structurant malheureusement. Il s'impose et il devient comme cela une sorte d'objet... », 2025

Thierry VERDIER
Directeur de l'ENSAM